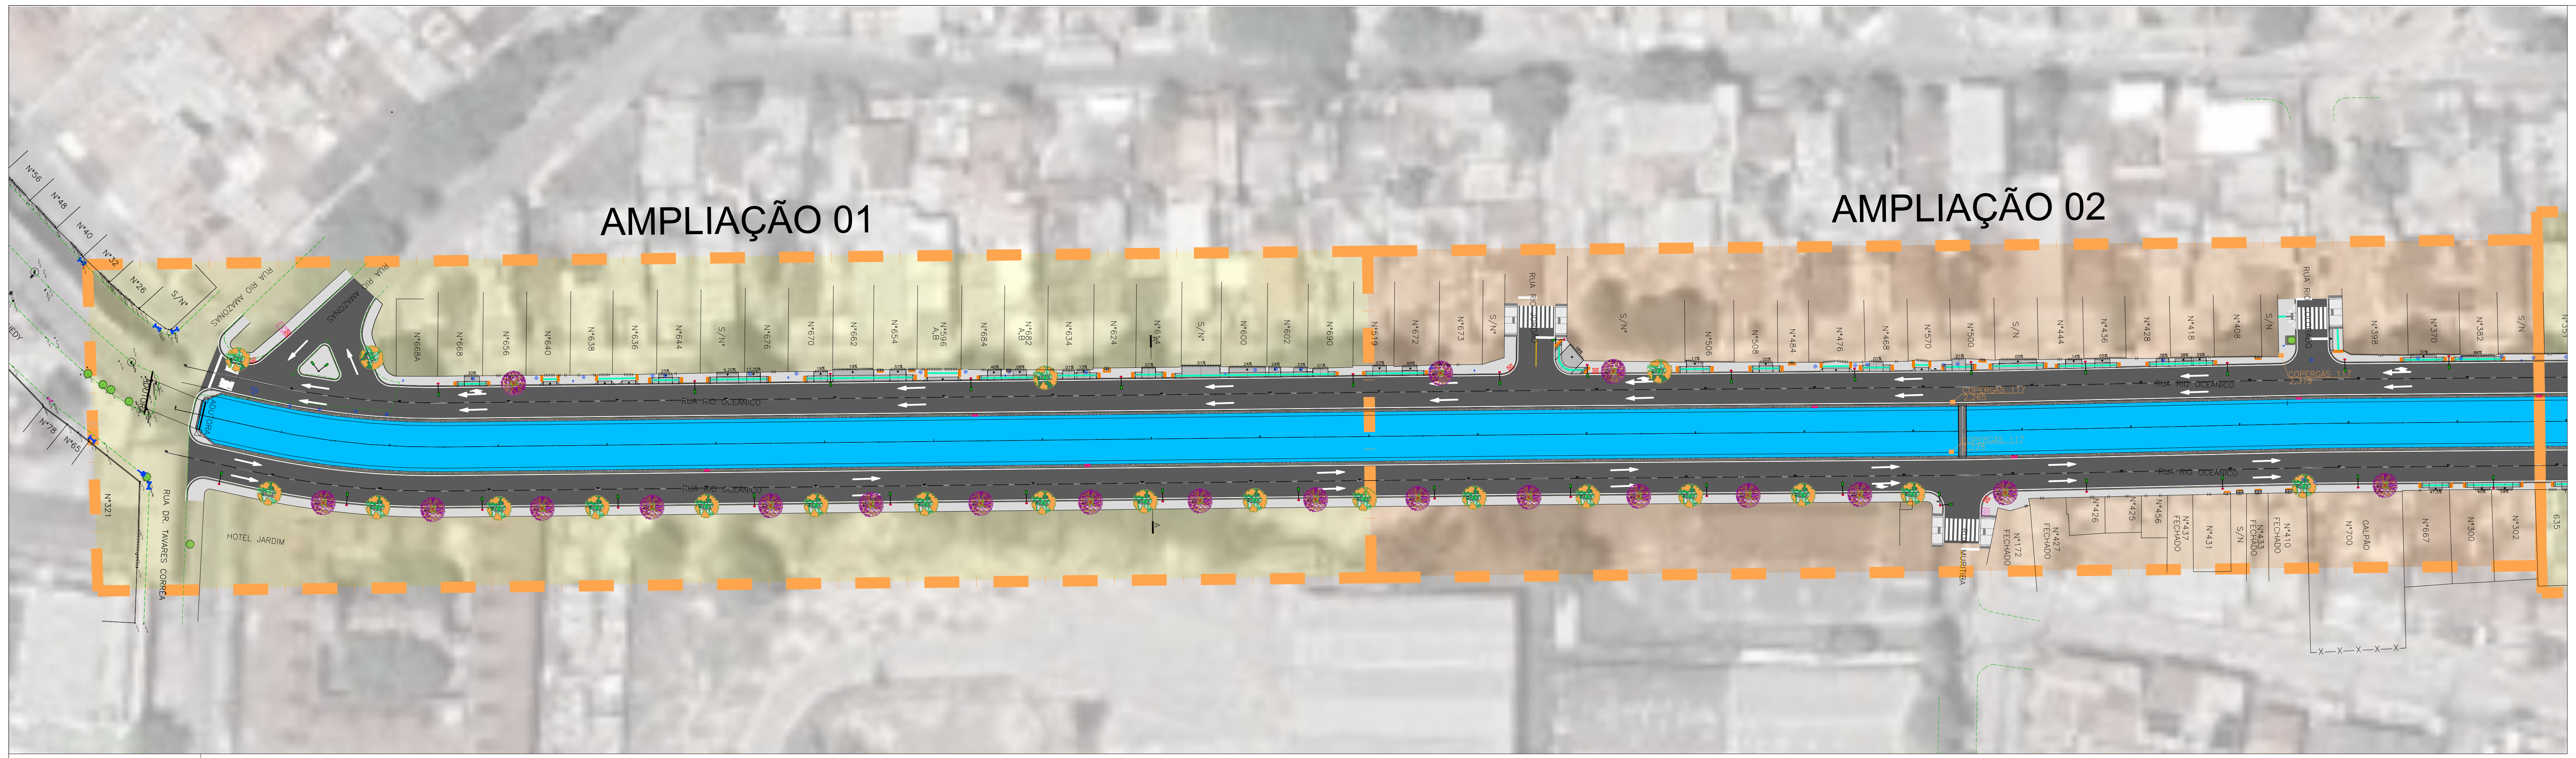

PLANTA BAIXA
ESCALA 1/750

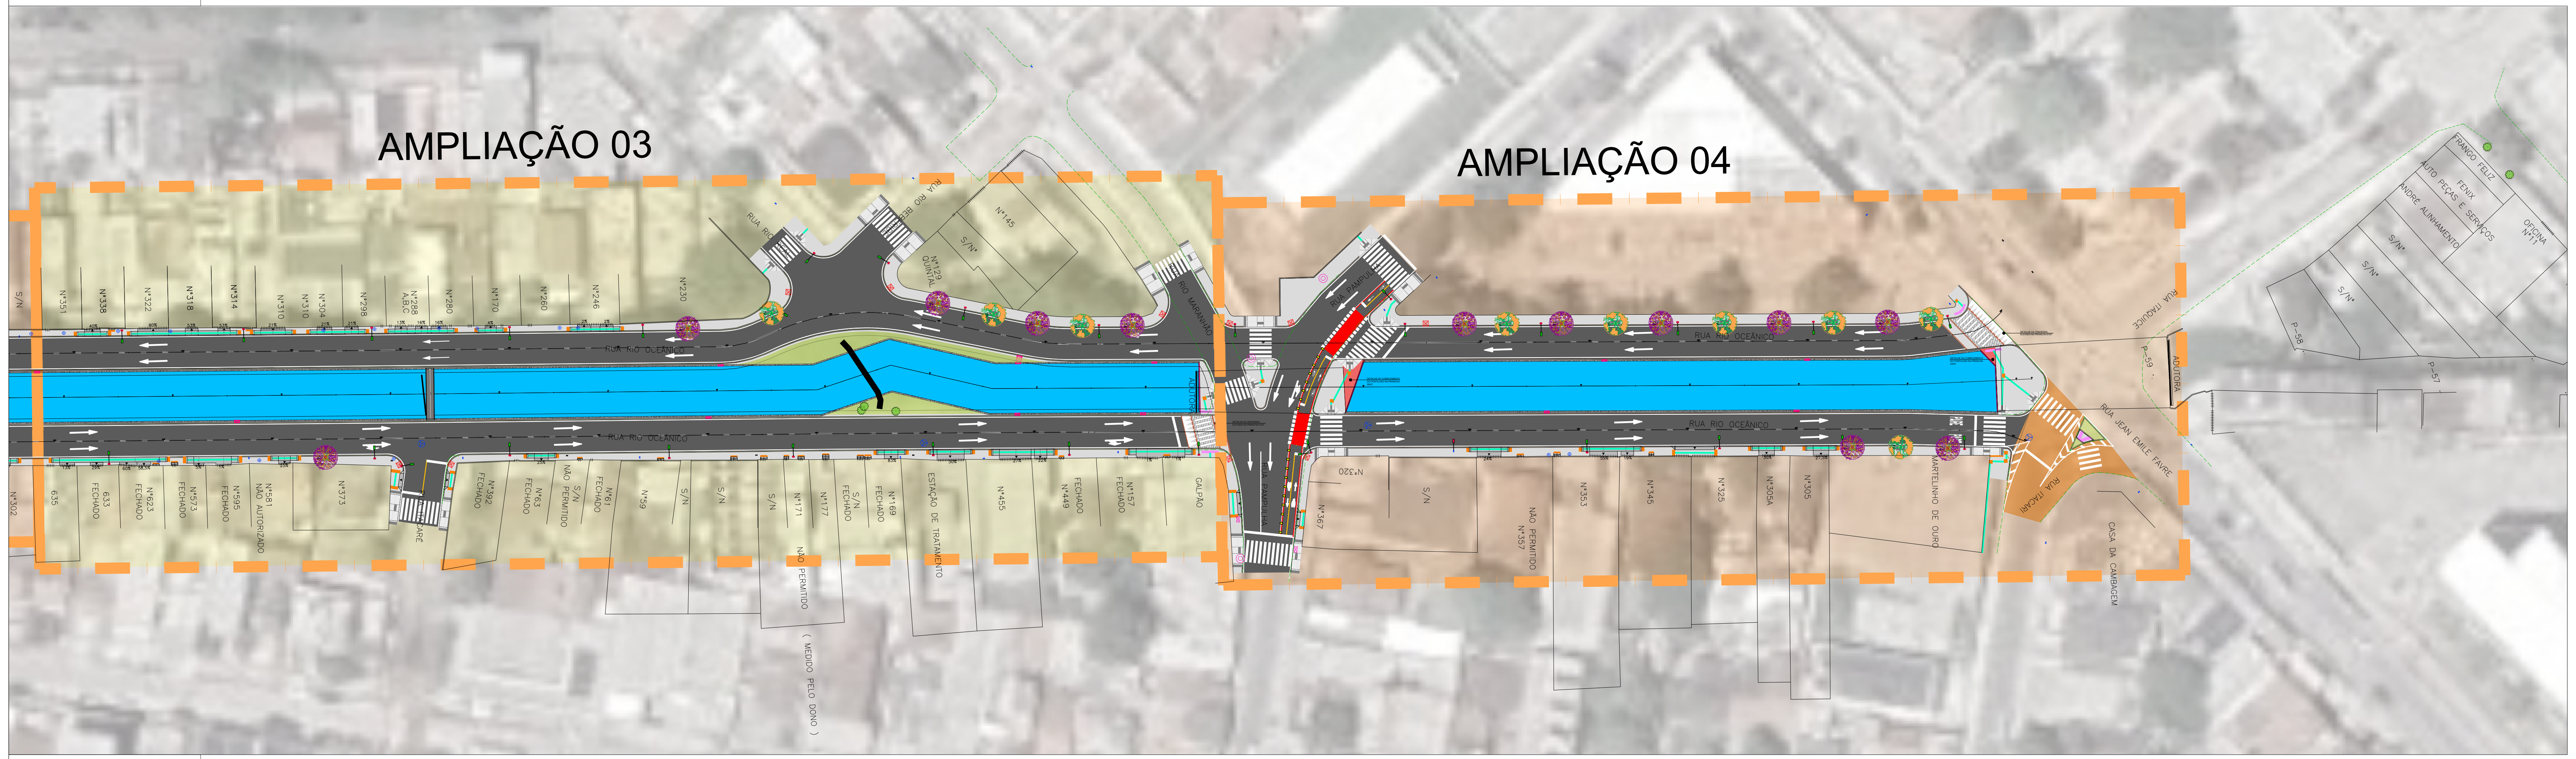

PLANTA BAIXA
ESCALA 1/750

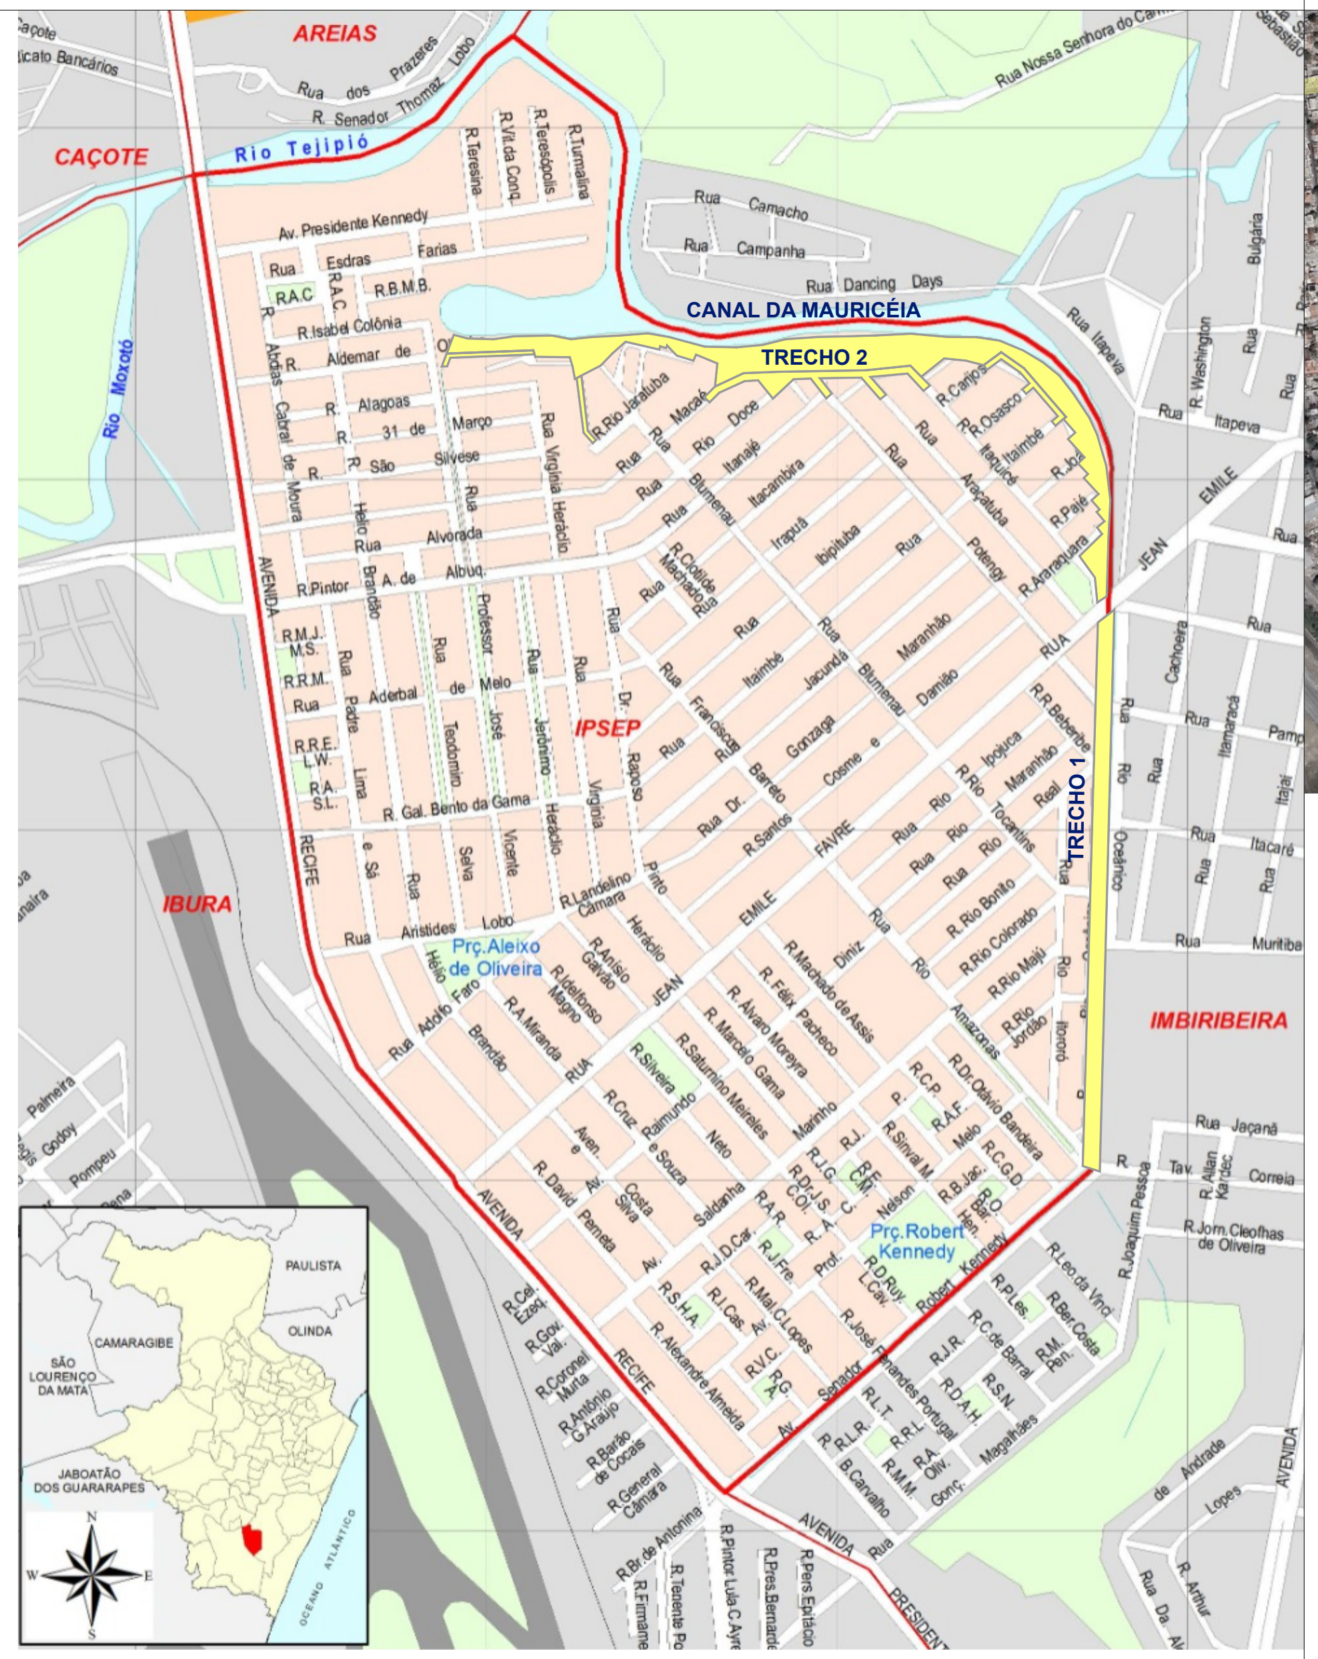

CANAL DA MAURICÉIA - TRECHO 01
PLANTA DE LOCALIZAÇÃO DA ÁREA DE INTERVENÇÃO
SEM ESCALA

CANAL DA MAURICÉIA - TRECHO 01
PLANTA DE LOCALIZAÇÃO DA ÁREA DE INTERVENÇÃO
SEM ESCALA

QUADRO DE QUANTIDADES
(VER DETALHE NAS PRANCHAS 06/07)

ITEM	NOME	QUANT. AMP. 01	QUANT. AMP. 02	QUANT. AMP. 03	QUANT. AMP. 04	QUANT. TOTAL
▬	GUARDA-CORPO EM FERRO GALVANIZADO , COM ALTURA H=0,80m, SOBRE MURETA EM ALVENARIA, H=0,30 EM RELAÇÃO À COTA DO PISO.	-- m	-- m	9,10 m	21,98 m	31,08 m
▦	PISO TÁTIL ALERTA, DE CONCRETO, PARA DEFICIENTES VISUAIS 40X40 CM	-- m²	11,95 m²	16,76 m²	19,53 m²	48,24 m²
▦	PISO TÁTIL ALERTA, DE CONCRETO, PARA DEFICIENTES VISUAIS 25 X 25 CM	30,55 m²	30,16 m²	25,17 m²	19,34 m²	105,22 m²
▥	PISO TÁTIL DIRECIONAL, DE CONCRETO, PARA DEFICIENTES VISUAIS 25 X 25 CM	26,71 m²	28,26 m²	38,66 m²	24,65 m²	118,28 m²
═	ASSENTAMENTO DE GUIA (MEIO-FIO) EM TRECHO RETO, CONFECCIONADA EM CONCRETO PRÉ-FABRICADO, DIMENSÕES 80X10X10X30 CM (COMPRIMENTO X BASE INFERIOR X BASE SUPERIOR X ALTURA), PARA VIAS URBANAS (ALEGRETES)	57,45 m	41,30 m	18,38 m	29,87 m	147,00 m
▭	PISO DE CONCRETO MOLDADO IN LOCO, USINADO, ACABAMENTO CONVENCIONAL	874,65 m²	828,72 m²	875,82 m²	850,21 m²	3.429,40 m²
⊢⊣	RAMPA ACESSÍVEL PARA PEDESTRES - TIPO 2; VER DETALHES NA PRANCHA 06/07.	-- unid.	05 unid.	06 unid.	06 unid.	17 unid.
△	RAMPA ACESSÍVEL PARA PEDESTRES - TIPO 1; VER DETALHES NA PRANCHA 06/07.	-- unid.	01 unid.	03 unid.	08 unid.	12 unid.

OBSERVAÇÕES: O QUANTITATIVO DO MEIO FIO DAS VIAS ENCONCTRAM-SE NO PROJETO DE PAVIMENTAÇÃO .

QUADRO DE PAISAGISMO

CÓDIGO	ITEM	NOME POPULAR	NOME CIENTÍFICO	ALTURA MÉDIA (m)	TAMANHO MUDA (m)	DIÂMETRO COPA (m)	ESPAÇAMENTO	QUANT. AMP. 01	QUANT. AMP. 02	QUANT. AMP. 03	QUANT. AMP. 04	QUANT. TOTAL
PN	🟩	GRAMA BATATAIS	*Paspalum notatum*	-	placas (40x60)cm	-	Placas assentadas lado a lado	11,25 m²	8,75 m²	175,71 m²	14,49 m²	210,20 m²
TG	●	QUARESMEIRA	*Tibouchina granulosa*	4.00m a 5.00m	0,50m	7.00m	3.00m	11 unid.	09 unid.	05 unid.	07 unid.	32 unid.
TP	●	ALGODÃO DA PRAIA	*Talipariti Pernambucense*	3.00m a 6.00m	0,15m	4.00m	3.00m	14 unid.	07 unid.	03 unid.	06 unid.	30 unid.
	●	ÁRVORE EXISTENTE										

LEGENDA

■	VIA DE VEÍCULOS PROPOSTA - 6,00m
▭	CALÇADA PROPOSTA
▨	COMPLEMENTO DA LAJE DO PONTILHÃO DA RUA PAMPULHA E RUA JEAN EMILE FAVRE
■	ÁREA DE PAVIMENTO EXISTENTE A SER MANTIDO, CONSIDERAR APENAS SINALIZAÇÃO HORIZONTAL PROJETADA
🟦	REPRESENTAÇÃO DO CANAL
━	LINHA LIMITE DA AMPLIAÇÃO
▭	EDIFICAÇÃO
- - -	MEIO-FIO EXISTENTE
E	EIXO
┼┼┼	PORTÃO/ GRADE
━	ADUTORA
●	ÁRVORE EXISTENTE
● ●	ÁRVORE PROPOSTA
┳	PLACA DE SINALIZAÇÃO
⊕	CAIXA DE PASSAGEM DE ESGOTO CONDOMINIAL EXISTENTE
○	POÇO DE VISITA DE ESGOTO EXISTENTE
▢	POÇO DE VISITA TIPO GAVETA EXISTENTE
▬	ENTRADA DE ÁGUA PROJETADA
☒	POÇO DE VISITA TIPO GAVETA PROJETADO
─■	LUMINÁRIA FECHADA TIPO PÉTALA, 120W, MODELO CLP-A(F), MARCA CONEXLED OU SIMILAR, COM BRAÇO DE 1,50M, CONFORME PROJETO DE ILUMINAÇÃO
●	POSTE DE CONCRETO DUPLO "T", DE $^{600}/_{9}$, A SER INSTALADO.
⊢⊣	POSTE DE CONCRETO DUPLO T, BAIXA TENSÃO, NEOENERGIA- PE EXISTENTE A SER MANTIDO
▲	RAMPA PARA ACESSO DE VEÍCULOS PROPOSTA
02 01	ESCADA/ DEGRAU DE ACESSO PROPOSTA AS EDIFICAÇÕES
△	RAMPA ACESSÍVEL PARA PEDESTRES - TIPO 1
⊢⊣	RAMPA ACESSÍVEL PARA PEDESTRES - TIPO 2
▬	PASSARELA

NOTAS/ OBSERVAÇÕES:

*SUGERE-SE REALIZAR UM COMPLEMENTO DA LAJE DO PONTILHÃO LOCALIZADO NA RUA JEAN EMILE FAVRE E NA RUA PAMPULHA, CONFORME DETALHE NA PRANCHA 05/07, PARA VIABILIZAR A ROTA ACESSÍVEL DA ÁREA DE INTERVENÇÃO.

*AS RAMPAS PARA ACESSO DE VEÍCULOS 1 E 2, CUJO OS DETALHES ENCONTRAM-SE NA PRANCHA 06/07, FORAM DESENVOLVIDAS PARA O PROJETO EM QUESTÃO DE MODO A GARANTIR QUE HAJA UMA FAIXA LIVRE DE CIRCULAÇÃO MÍNIMA DE PEDESTRE DE 90 CM, TENDO O PISO ALERTA DUPLO LOCALIZADO NO INÍCIO E NO FIM DO PERCURSO.

* DEVIDO ÀS CONDIÇÕES DE INFRAESTRUTURA LOCAL, EM ALGUNS TRECHOS NÃO SERÁ POSSÍVEL ATENDER AS NORMAS DE ACESSIBILIDADE.

*O QUANTITATIVO CORRESPONDENTE AO PISO DE CONCRETO MOLDADO IN LOCO, CONSIDERA A SOMA DOS PISOS DAS CALÇADAS E DAS RAMPAS TIPO 01, 02 PARA ACESSO DE VEICULO E DE ACESSIBILIDADE.

*O QUANTITATIVO CORRESPONDENTE ÀS PASSARELAS SERÁ APRESENTADO NA PRANCHA DE ESTRUTURA.

JULHO/2025	R03	ACRECIMO DE TRAVESSIA SOBRE O CANAL, A PEDIDO DA URB RECIFE
MAIO/2025	R02	AJUSTES CONFORME ANÁLISE DISPONÍVEL NO DOCS, RECEBIDA EM 22/05/2025
MAIO/2025	R01	AJUSTES CONFORME ANÁLISE GPU-AN-18032025, RECEBIDA EM 18/03/2025
2025	R00	EMISSÃO INICIAL
DATA	REVISÃO	DESCRIÇÃO

URB RECIFE
PREFEITURA DA CIDADE DO RECIFE
SECRETARIA DE INFRAESTRUTURA
AUTARQUIA DE URBANIZAÇÃO DO RECIFE

PREFEITURA DO
RECIFE

DIRETORA DE PLANEJAMENTO E PROJETOS	GERENTE GERAL DE PROJETOS DE INFRAESTRUTURA	GERENTE GERAL DE PROJETOS URBANOS
LUANA GENTIL	DÂMARIS TAVARES	MARIANA AFONSO FERREIRA

PROJETOS EXECUTIVOS DE URBANISMO, PAISAGISMO, ARQUITETURA E COMPLEMENTARES DE ENGENHARIA PARA O CANAL DA MAURICÉIA

PROJETO :
PROJETO EXECUTIVO DE URBANISMO, PAISAGISMO E ARQUITETURA

LOCAL :
IPSEP, RECIFE-PE

CONTEÚDO :
TRECHO 01 - IMPLANTAÇÃO GERAL

ESCALA :
INDICADA

DATA :
JULHO/2025

RESPONSÁVEL TÉCNICO GERAL:

ARQ. DIGITAL:
P01.TRECHO 1-CMAUR-URB-ImplGeral.dwg

EQUIPE TÉCNICA

PROPRIETÁRIO

RESPONSÁVEL TÉCNICO