PLANTA - CHAVE
ESCALA 1/1000

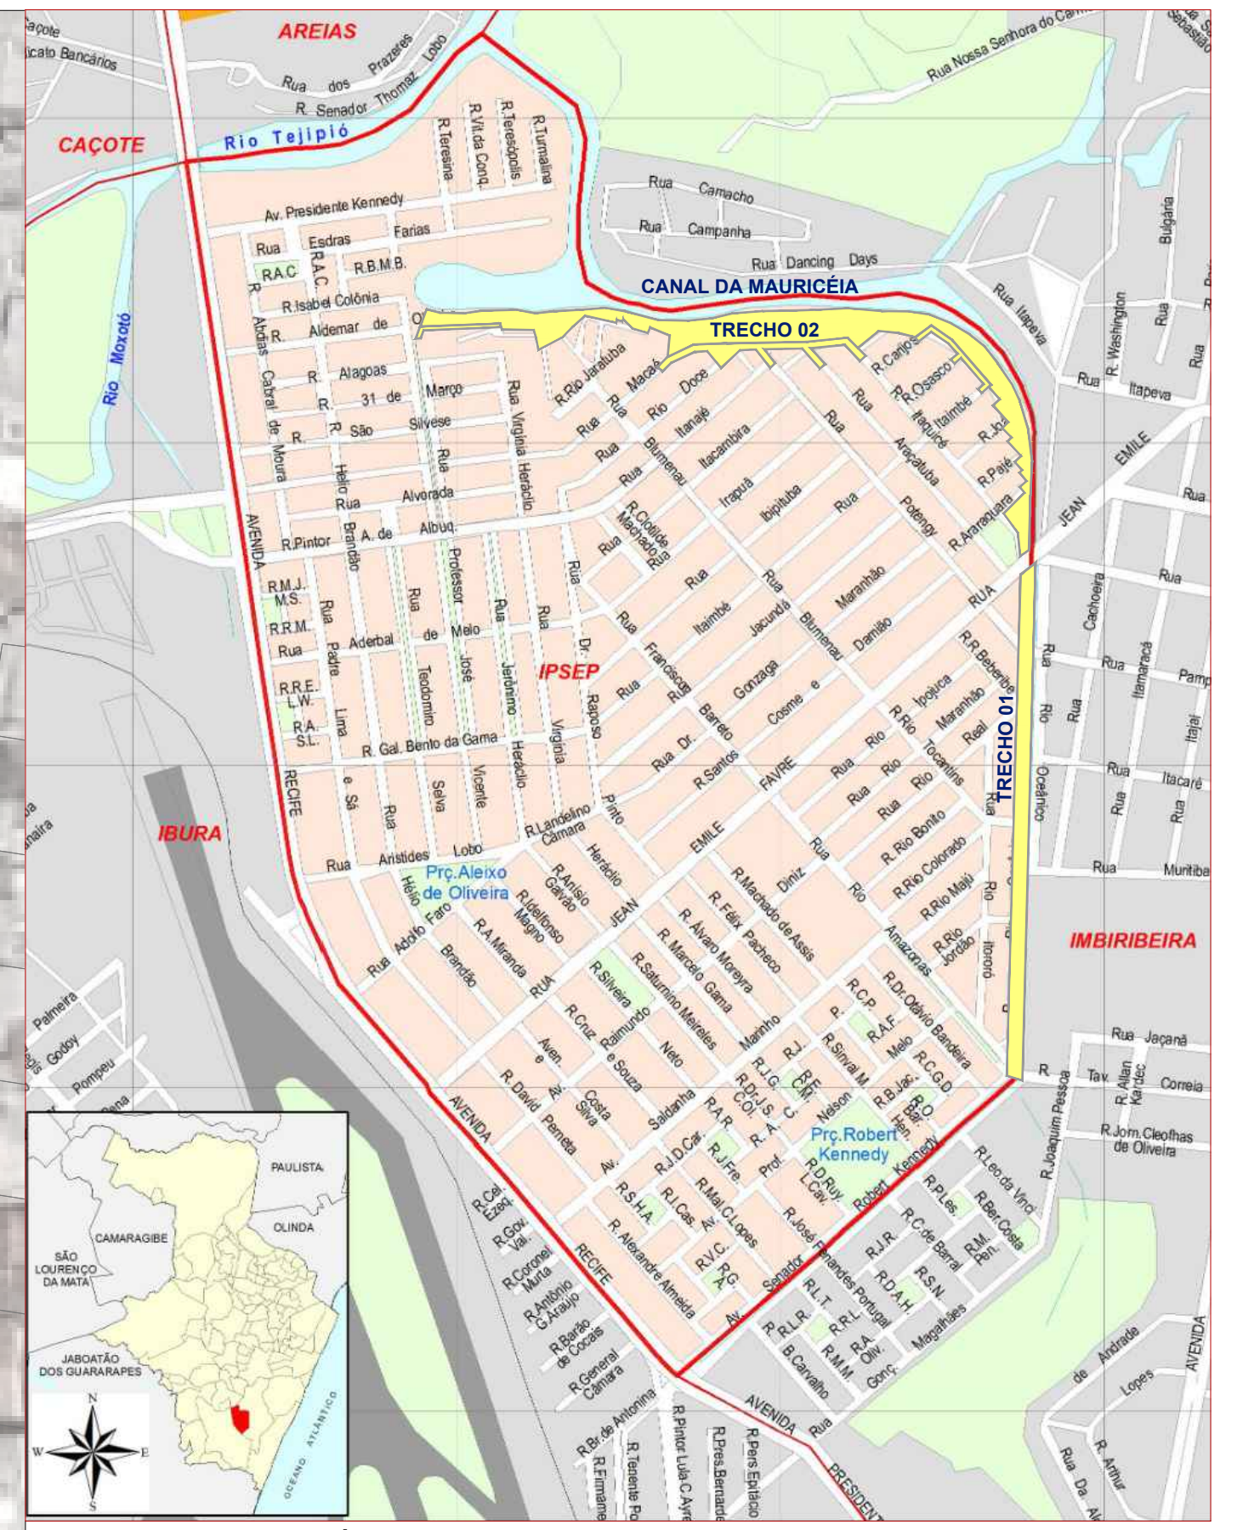

CANAL DA MAURICÉIA - TRECHOS 01 E 02
PLANTA DE LOCALIZAÇÃO DA ÁREA DE INTERVENÇÃO
SEM ESCALA

AGENCIAMENTO - QUANTITATIVO GERAL

QUADRO DE PISOS EXTERNOS

ITEM	ESPECIFICAÇÕES	QUANT.
▨	BLOCO INTERTRAVADO DE CONCRETO, ASSENTAMENTO TIPO ESPINHA DE PEIXE, DIMENSÕES 10X20CM, COR CINZA NATURAL, ESPESSURA 6CM,ASSENTADO SOBRE COLCHÃO DE AREIA COM 5CM E BASE REGULARIZADA	758,05 m²
▨	BLOCO INTERTRAVADO DE CONCRETO, ASSENTAMENTO TIPO ESPINHA DE PEIXE, DIMENSÕES 10X20CM, COR CINZA GRAFITE, ESPESSURA 6CM,ASSENTADO SOBRE COLCHÃO DE AREIA COM 5CM E BASE REGULARIZADA	--
🟨	BLOCO INTERTRAVADO DE CONCRETO, ASSENTAMENTO TIPO ESPINHA DE PEIXE, DIMENSÕES 10X20CM, COR AMARELO OCRE, ESPESSURA 6CM,ASSENTADO SOBRE COLCHÃO DE AREIA COM 5CM E BASE REGULARIZADA	634,16 m²
🟥	BLOCO INTERTRAVADO DE CONCRETO, ASSENTAMENTO TIPO ESPINHA DE PEIXE, DIMENSÕES 10X20CM, COR VERMELHO, ESPESSURA 6CM,ASSENTADO SOBRE COLCHÃO DE AREIA COM 5CM E BASE REGULARIZADA	-- m²
▨	BLOCO INTERTRAVADO DE CONCRETO, ASSENTAMENTO TIPO ESPINHA DE PEIXE, DIMENSÕES 10X20CM, COR GRAFITE, ESPESSURA 8CM,ASSENTADO SOBRE COLCHÃO DE AREIA COM 5CM E BASE REGULARIZADA	VER PROJ. GEOMÉTRICO
▨	PISO EM PLACAS DRENANTE FULGET, COM ACABAMENTO LIXADO, NAS DIMENSÕES 20X40X8CM, NA COR GRAFITE, RESISTÊNCIA 35 MPA, ASSENTAMENTO TIPO ESPINHA DE PEIXE. REF.: CONCREPOXI OU SIMILAR	155,13 m²
⬜	CONCRETO MOLDADO IN LOCO, USINADO, ACABAMENTO CONVENCIONAL, ESPESSURA 6CM	2.345 m²
🟩🟥🟨🟦🟦🟧⬜	PISO DE BORRACHA RECICLADA DE PNEU DE ALTA PERFORMANCE, NAS CORES VERDE, VERMELHO, AMARELO, AZUL ESCURO, AZUL CLARO, LARANJA E BRANCO, COM UMA CAMADA SOBRE BASE EM SOLO COMPACTADO E SUB-BASE COM BRITA GRADUADA SIMPLES,MARCA PISOLEVE OU EQUIVALENTE TÉCNICO	297,93 m²
🟦	PINTURA EM TINTA ACRÍLICA NA COR AZUL SOBRE (CONCRETO MOLDADO IN LOCO, USINADO, ACABAMENTO CONVENCIONAL, ESPESSURA 6CM)	63,92 m²
🟫	AREIA COM ESPESSURA MÍNIMA DE 30CM	781,75 m²
🟩	GRAMA BATATAIS / JARDIM	2.519,58 m²
🟫	SOLO NATURAL	41,56 m²
▨	PISO EM MADEIRA ECOLÓGICA EM TÁBUA MACIÇA EM MADEIRA ECOLÓGICA (WPC)	249,63 m²
🟩	MEIO FIO EM CONCRETO PRÉ-FABRICADO PARA URBANIZAÇÃO, TRECHO CURVO, INSTALADO NO NÍVEL DO PISO EXTERNO	551,4 m
🟧	MEIO FIO EM CONCRETO PRÉ-FABRICADO PARA URBANIZAÇÃO, TRECHO CURVO, INSTALADO A 5CM DO NÍVEL DO PISO EXTERNO	
🟪	MEIO FIO EM CONCRETO PRÉ-FABRICADO PARA URBANIZAÇÃO, TRECHO RETO, INSTALADO NO NÍVEL DO PISO EXTERNO	1.597,59 m
🟦	MEIO FIO EM CONCRETO PRÉ-FABRICADO PARA URBANIZAÇÃO, TRECHO RETO, INSTALADO A 5CM DO NÍVEL DO PISO EXTERNO	
⬜	PISO PODOTÁTIL DE ALERTA, DE CONCRETO, ASSENTADO SOBRE ARGAMASSA, DIMENSÕES 25 X 25 X 2,5CM	VER PROJ. ACESSIB.
🟪	PISO PODOTÁTIL DE ALERTA, DE CONCRETO, ASSENTADO SOBRE ARGAMASSA, DIMENSÕES 40 X 40 X 2,5CM	VER PROJ. ACESSIB.
🟩	PISO PODOTÁTIL DIRECIONAL , DE CONCRETO, ASSENTADO SOBRE ARGAMASSA, DIMENSÕES 25 X 25 X 2,5CM	VER PROJ. ACESSIB.

QUADRO DE MOBILIÁRIO URBANO

ITEM	NOME	QUANT.
A1	RAMPA ACESSÍVEL PARA PEDESTRES - TIPO 2 COM PISO TÁTIL EM PLACA DE CONCRETO PRÉ-MOLDADO	VER PROJ. ACESSIB.
A2	RAMPA ACESSÍVEL PARA PEDESTRES - TIPO 1 COM PISO TÁTIL EM PLACA DE CONCRETO PRÉ-MOLDADO	VER PROJ. ACESSIB.
A3	MESA DE CONCRETO COM 60CM E BANCOS REDONDOS EM CONCRETO	33 unid.
A4	MESA DE CONCRETO COM 90CM E BANCOS REDONDOS EM CONCRETO - ACESSIBILIDADE	08 unid.
A5	ALEGRETE-BANCO REDONDO DE CONCRETO ARMADO, ESTRUTURADO EM BASE DE ALVENARIA DE 1 VEZ.	09 unid.
A6	ALEGRETE EM CONCRETO PRÉ-MOLDADO INSTALADO NO NÍVEL DO PISO	08 unid.
A7	LIXEIRA EM ESTRUTURA DE AÇO GALVANIZADO E RIPAS DE MADEIRA MACIÇA TRATADA E ENVERNIZADA	21 unid.
A8	BANCO DE CONCRETO ARMADO DE 5 METROS ESTRUTURADO EM BASE DE ALVENARIA DE 1 VEZ	13 unid.
A8.1	BANCO DE CONCRETO ARMADO DE 3 METROS ESTRUTURADO EM BASE DE ALVENARIA DE 1 VEZ	09 unid.
A9	GUARDA-CORPO EM FERRO GALVANIZADO PINTADO COM TINTA EPÓXI, H=1.00m, SOBRE MURETA DE CONCRETO.	245,42 m
A9.1	CORRIMÃO EM FERRO GALVANIZADO PINTADO COM TINTA EPÓXI (RAMPA).	77,77m
A9.2	GUARDA-CORPO EM FERRO GALVANIZADO PINTADO COM TINTA EPÓXI, H=1,10m (RAMPA).	85,67m
A9.3	GUARDA-CORPO EM FERRO GALVANIZADO FIXADO EM PILARETE DE CONCRETO COM CHAPA METÁLICA E PARABOLT Ø3/8", H=1.10m. UTILIZAR SOLDA ESPECÍFICA PARA PEÇA GALVANIZADA (PIER).	60,89m
A10	ALAMBRADO DE TUBO GALVANIZADO COM MALHA QUADRADA 80X80 MM FIO 12 BWG, REVESTIDA DE PVC.	62,70 m
A12	BALIZADOR EM POLIETILENO, NA COR PRETA COM FAIXAS REFLETIVAS AMARELAS, 94CM DE ALTURA X 10CM DIÂMETRO	03 unid.
A14	MESA MODULAR COM ASSENTOS INTEGRADOS, ESTRUTURA EM AÇO CARBONO E TAMPO DA MESA E ASSENTOS EM MADEIRA MACIÇA NATURAL, CONJUNTO PICNIC, REF. AIR-L, METALCO OU SIMILAR	11 unid.
A15	ALEGRETE RETANGULAR 1 EM CONCRETO PRÉ-MOLDADO INSTALADO NO NÍVEL DO PISO, 0,45x1,00M	03 unid.
A16	ALEGRETE RETANGULAR 2 EM CONCRETO PRÉ-MOLDADO INSTALADO NO NÍVEL DO PISO, 0,90X1,00M	-- unid.

NOTA: O QUANTITATIVO E DETALHAMENTO DE PISOS TÁTEIS E DE RAMPAS ACESSÍVEIS TIPO 1 E TIPO 2 ESTÃO APRESENTADOS NA PRANCHA DE ACESSIBILIDADE (P03/19).

QUADRO DE BRINQUEDOS PARA PARQUE INFANTIL

ITEM	NOME	QUANT.
B1	ESCORREGO EM MADEIRA DE EUCALIPTO E ALÇA METÁLICA, MEDIDAS 2,83m x 1,84m x 0,50m	03 und.
B2	BALANÇO DE 3 LUGARES EM MADEIRA DE EUCALIPTO FIXADO COM CORDAS, 3,20 X 2,50m	--
B3	GANGORRA DUPLA EM MADEIRA DE EUCALIPTO E ALÇA METÁLICA, 2,90 X 0,95m	05 und.
B4	GIRA-GIRA INCLUSIVO EM TUBO DE AÇO CARBONO COM SUPERFÍCIE LISA E CANTOS ARREDONDADOS, DIÂMETRO 2,00M	02 und.
B8	MORRO COM ESCALADA EM EPDM COM ALTURAS VARIÁVEIS (CONJUNTO COM 3 UNIDADES)	04 und.
B9	BALANÇO DUPLO COM ESCALADA EM MADEIRA DE EUCALIPTO, MEDIDAS 3,57m x 2,52m.	02 und.
B11	PULA PULA DE PISO - Ø1.00m	05 und.
B12	AMARELA: PINTURA PARA PISO EPÓXI, NAS CORES VERMELHO, AZUL CLARO, LARANJA E VERDE COM TEXTO NA COR PRETO, SOBRE PISO DE INTERTRAVADO OU PISO CIMENTADO*.	05 und.
B16	CARACOL NUMÉRICO: PINTURA PARA PISO EPÓXI, NAS CORES LARANJA, AZUL ESCURO, AMARELO E VERDE, COM TEXTO NA COR BRANCA, SOBRE PISO DE INTERTRAVADO OU PISO CIMENTADO*.	02 und.

* **NOTA:** PARA OS BRINQUEDOS INSTALADOS EM PISO DE BORRACHA, ADOTAR A MESMA ESPECIFICAÇÃO DO PISO EMBORRACHADO UTILIZANDO AS CORES CORRESPONDENTES.

QUADRO DE EQUIPAMENTOS DE ACADEMIA

ITEM	NOME	QUANT.
C1	PRANCHA PARA EXERCÍCIOS ADBDOMINAIS EM CONCRETO PRÉ-MOLDADO	03 und.
C2	BICICLETA DE MÃO PARA PESSOAS COM DEFICIÊNCIA (PCD) EM TUBO DE AÇO	--
C3	APARELHO BARRAS PARALELAS RETANGULAR EM AÇO INOXIDÁVEL, CHAPAS DE ESPESSURA E=4mm, COM COLUNAS DE 100mm X 50mm, TUBOS DE Ø50,8mm. ACABAMENTO POLIDO.	02 und.
C4	APARELHO BARRAS FIXAS EM AÇO INOXIDÁVEL, CHAPAS DE ESPESSURA=4mm, ACABAMENTO POLIDO	01 und.
C5	ESTAÇÃO DE MUSCULAÇÃO EM AÇO INOXIDÁVEL, COM ESTRUTURA TUBULAR 80mm X 80mm E 50mm X 30mm, DE ESPESSURA E=4mm, ACABAMENTO POLIDO.	01 und.

** **NOTA:** BANCO REVESTIDO EM COURO FEITO DE FILME PVC COM REFORÇO DE POLIÉSTER, ESPESSURA 0,4mm COM ACABAMENTO EM TEFLON E TRATAMENTOS UV, ANTI-CHAMAS E ANTI-FUNGOS.

QUADRO DE ILUMINAÇÃO PÚBLICA

	POSTE DE ILUMINAÇÃO COM 2 LUMINÁRIAS LED PARA ILUMINAÇÃO PÚBLICA, 50W CADA, MODELO GIRAFA, SONERES OU SIMILAR - ALTURA 5M, CONFORME PROJETO DE ILUMINAÇÃO	VER PROJ. ILUMINA.
	LUMINÁRIA EM LED PARA ILUMINAÇÃO PÚBLICA, 50W, BIVOLT, LENTE EM POLICARBONATO, CORPO EM ALUMÍNIO, MODELO GIRAFA DA SONERES OU SIMILAR, INSTALADO EM POSTE DE ALUMÍNIO RETO DE 5 METROS ÚTEIS, ENGASTADO.	
	LUMINÁRIA EM LED PARA ILUMINAÇÃO PÚBLICA, 100W, CORPO EM ALUMÍNIO, EM POSTE CÔNICO DE 7 METROS ÚTEIS, FLANGEADO.	
	DUAS LUMINÁRIA EM LED PARA ILUMINAÇÃO PÚBLICA, 100W CADA, CORPO EM ALUMÍNIO, EM POSTE CÔNICO DE 7 METROS ÚTEIS, FLANGEADO.	
	POSTE RETO DE AÇO CÔNICO DE 7 METROS ÚTEIS, ENGASTADO, COM UM PROJETOR EM LED DE 150W CADA, MYROS 3, DA MARCA SONERES OU SIMILAR.	
🟦	POSTE DE CONCRETO DUPLO T , DE $^{400}/_{9}$, A SER INSTALADO.	

QUADRO DE PAISAGISMO

CÓDIGO	ITEM	NOME POPULAR	NOME CIENTÍFICO	ALTURA MÉDIA (m)	TAMANHO MUDA (m)	ESPAÇAMENTO	DIÂMETRO COPA (m)	QUANT.
BM		PATA DE VACA	*Bauhinia monandra*	5.00m a 7.00m	2.50m	5.00m	4.00m	19 unid.
IM		INGÁ-FEIJÃO	*Inga marginata*	8.00m a 10.00m	2.50m	6.00m	5.00m	07 unid.
TU		IPE AMARELO	*Tabebuia umbellata*	10.00m a 15.00m	2.50m	8.00m	7.00m	43 unid.
TA		IPE ROXO	*Tabebuia avellanadae*	20.00m a 30.00m	2.50m	8.00m	8.00m	16 unid.
DT		DIANELA	*Dianella tasmanica*	0.70m	0.40m (muda cheia)	0.40m (6un/m²)	-	186 unid.
HP		HELICÔNIA PAPAGAIO	*Helicônia psittacorun*	1.50m a 2.00m	0.70m	0.40m (6un/m²)	-	67 unid.
PN	🟩	GRAMA BATATAIS	*Paspalum notatum*	-	placas (40x60)cm	Placas assentadas lado a lado	-	2.519,58 m²
AE		ÁRVORE EXISTENTE						

CONVENÇÕES DA IMPLANTAÇÃO GERAL

▨	VIA DE PEDESTRIANIZADA PROPOSTA EM INTERTRAVADO - 4,00m
⬚	LIMITE DA ÁREA DE INTERVENÇÃO ÁREA = 14.131,13m²
☐	EDIFICAÇÃO
- - -	MEIO-FIO EXISTENTE
━	LIMITE DA AMPLIAÇÃO
●	ÁRVORE EXISTENTE
⊕	CAIXA DE PASSAGEM DE ESGOTO CONDOMINIAL EXISTENTE
○	POÇO DE VISITA DE ESGOTO EXISTENTE
☐	POÇO DE VISITA TIPO GAVETA EXISTENTE
▤	CAIXA COLETORA COM GRELHA PROJETADA (DIMENSÕES INTERNAS 0,40 x 0,72M - L x C)
☒	POÇO DE VISITA TIPO GAVETA PROJETADO (DIMENSÕES INTERNAS 1,21 x 1,21M - L x C)
⊞	CAIXA DE LIGAÇÃO PROJETADA (DIMENSÕES INTERNAS 1,00 x 1,00M - L x C)
▶	CAIXA DE INSPEÇÃO PROJETADA (DIMENSÕES INTERNAS 1,18 x 1,18M - L x C)
●	POÇO DE VISITA TIPO TAMPÃO PROJETADO (DIMENSÕES INTERNAS 1,18 x 1,18M - L x C)
→→→	DRENO SUBSUPERFICIAL
▥	CANALETA RETA COM TAMPA 0,30 X 0,30

NOTAS/ OBSERVAÇÕES:

VERIFICAR EM OBRA E ASSEGURAR A ENTRADA DE VEÍCULOS A TODOS OS LOTES AFETADOS PELO PROJETO URBANÍSTICO, BEM COMO ATENTAR PARA CONFLITOS ENTRE ÁRVORES A IMPLANTAR EM TAIS ACESSOS.

SET./2025	R04	AJUSTES APÓS DIMINUIÇÃO DA DESAPROPRIAÇÃO E DA MANCHA DE ABRANGÊNCIA
AGOSTO/2025	R03	AJUSTES APÓS DIMINUIÇÃO DA DESAPROPRIAÇÃO E DA MANCHA DE ABRANGÊNCIA
MAIO/2025	R02	AJUSTES CONFORME ANÁLISE DISPONÍVEL NO DOCS, RECEBIDA EM 22/05/2025
MAIO/2025	R01	AJUSTES CONFORME ANÁLISE GPU-AN-18032025, RECEBIDA EM 18/03/2025
2025	R00	EMISSÃO INICIAL
DATA	REVISÃO	DESCRIÇÃO

PREFEITURA DA CIDADE DO RECIFE
SECRETARIA DE INFRAESTRUTURA
AUTARQUIA DE URBANIZAÇÃO DO RECIFE

PREFEITURA DO RECIFE

DIRETORA DE PLANEJAMENTO E PROJETOS
LUANA GENTIL

GERENTE GERAL DE PROJETOS DE INFRAESTRUTURA
DÂMARIS TAVARES

GERENTE GERAL DE PROJETOS URBANOS
MARIANA AFONSO FERREIRA

PROJETOS EXECUTIVOS DE URBANISMO, PAISAGISMO, ARQUITETURA E COMPLEMENTARES DE ENGENHARIA PARA O CANAL DA MAURICÉIA

PROJETO :
PROJETO EXECUTIVO DE URBANISMO, PAISAGISMO E ARQUITETURA

LOCAL :
IPSEP, RECIFE-PE

CONTEÚDO :
TRECHO 02 - IMPLANTAÇÃO GERAL

ESCALA :
INDICADA

DATA :
SETEMBRO/2025

RESPONSÁVEL TÉCNICO GERAL:

ARQ. DIGITAL:
P01_URB-CM-IMPLGERAL.dwg

EQUIPE TÉCNICA

PROPRIETÁRIO

RESPONSÁVEL TÉCNICO

01/19